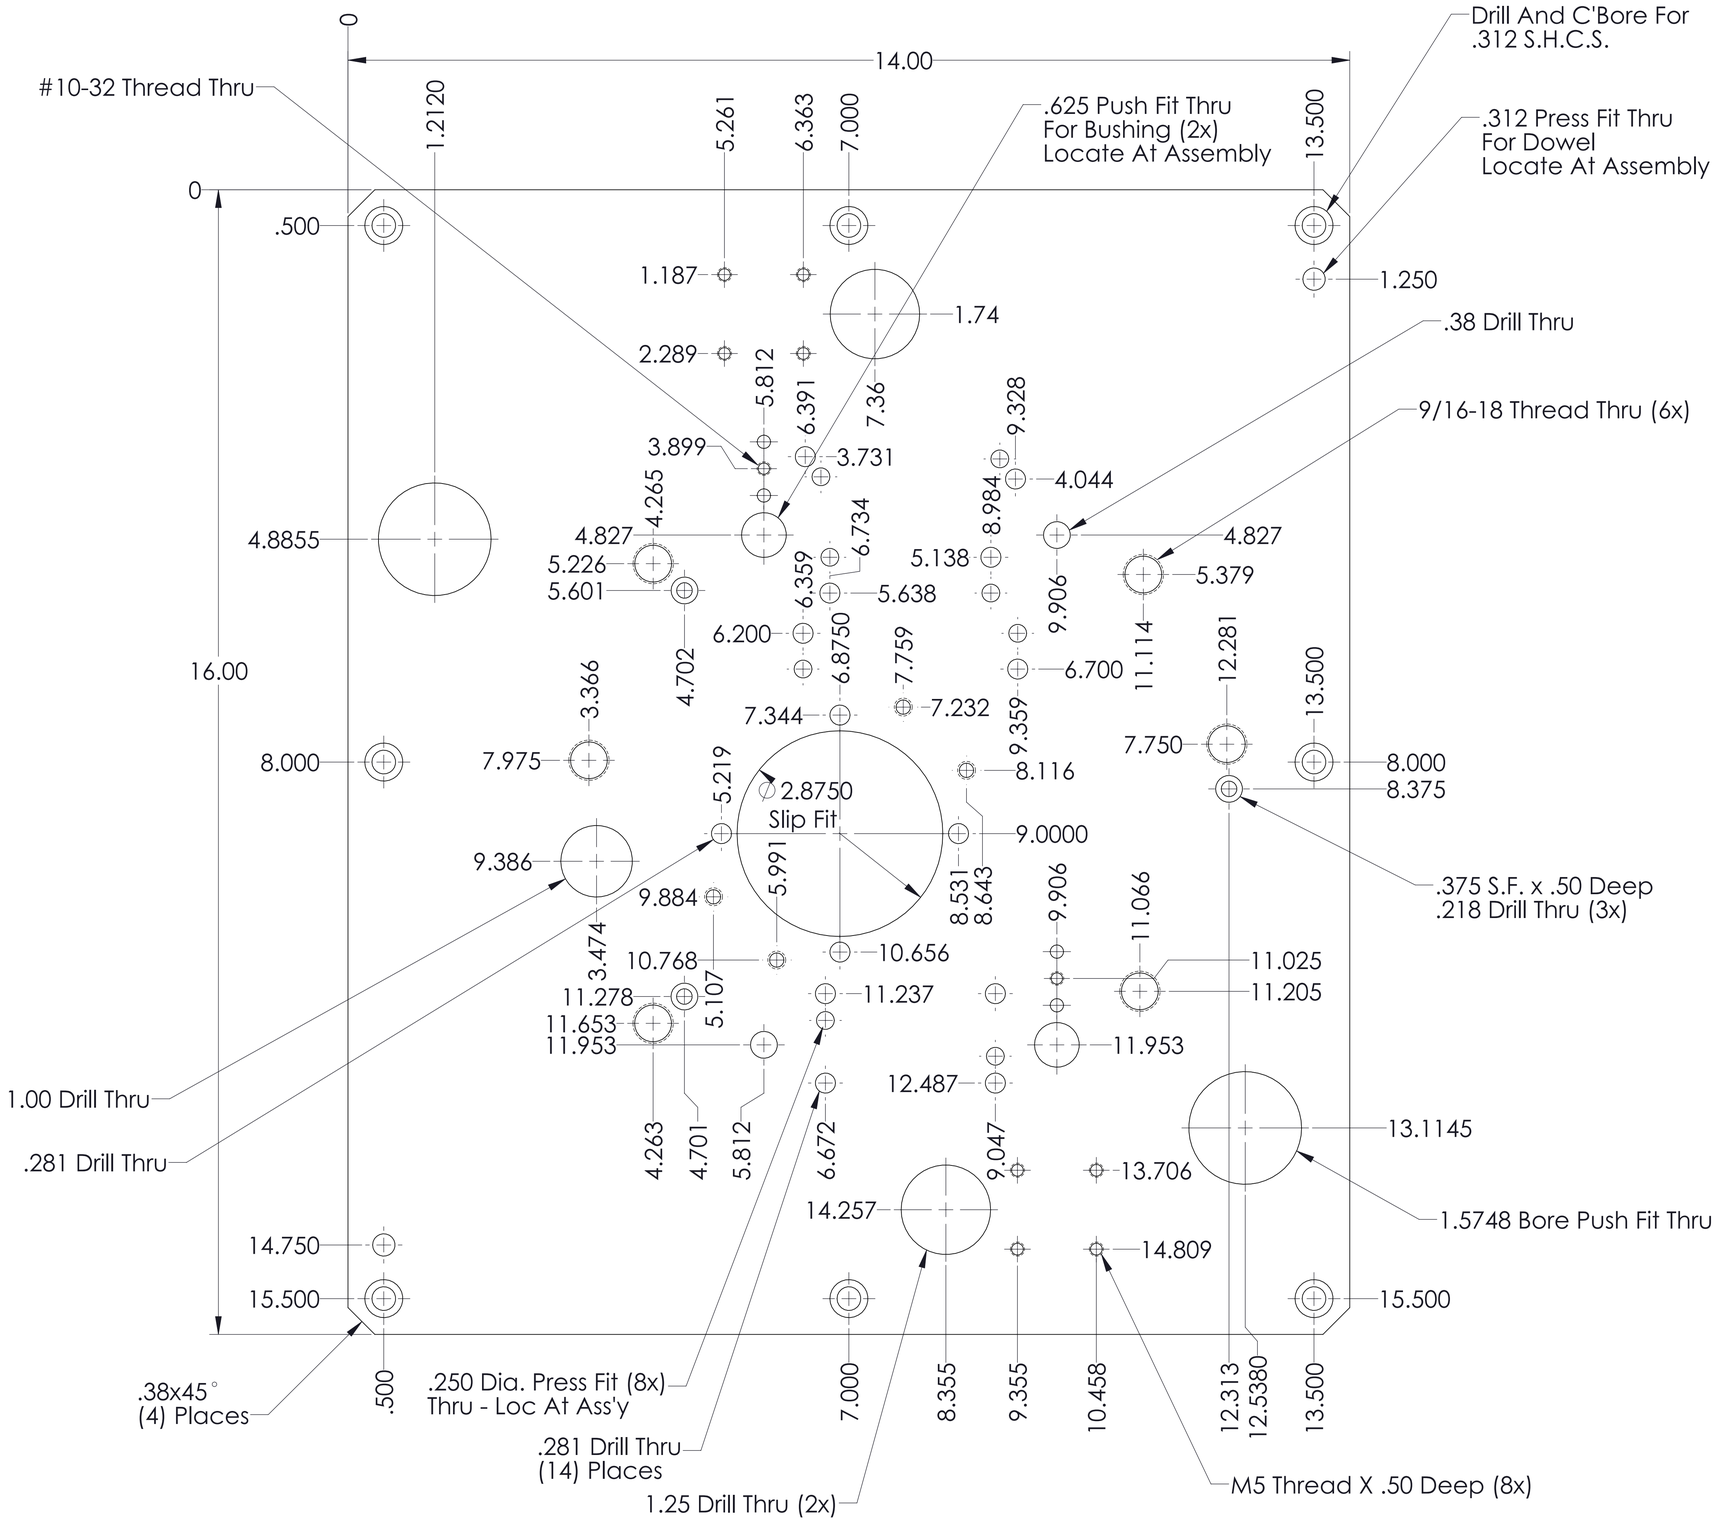


XX,XX,XX

# REQ'D: 1	DATE: 09/30/2015	56977 Elk Court Elkhart, IN 46516 Phone: (574) 522-9600 Fax: (574) 522-0685 Email: info@Jus-Rite.com Designers and Builders of Gages and Gage Fixtures
DUE:		Jus-Rite ENGINEERING, INC.
GAGE STAND: Y		

NOTE:
ALL DIMENSIONS MARKED THUS
ARE TO BE HELD ±.0005 UNLESS
OTHERWISE SPECIFIED & CERTIFIED

SCALE: FULL	P/N: 055	DRAWN BY: Brian
DATE: 9/25/15	P/P REV LETTER:	SHEET: 5 of
BUILT BY:	P/P REV DATE:	CAD FILE: 18592-005
CUSTOMER: Gibbs - Henderson		
TITLE: 055 Final Gage		DRAWING NUMBER: JRE 18592

JUS-RITE ENG. DESIGN D.O.# 18591 BUILD S.O.# 18592